


ELECTRICAL SCHEDULE			
SYMBOL	DESCRIPTION	MTG. HT.	REMARKS
	DUPLEX OUTLET	12" A.F.F., U.N.O.	
	GROUND FAULT INTERRUPTER	42" A.F.F., U.N.O.	
	WEATHER PROOF OUTLET	12" A.F.F., U.N.O.	TYP., AT ALL EXTERIOR LOCATIONS
	FLOOR OUTLET		VERIFY LOCATIONS W/ OWNER, TYP.
	DOUBLE DUPLEX OUTLET	12" A.F.F., U.N.O.	
	OUTLET- 220V		
	DUPLEX OUTLET W/ ONE PORT SWITCH CONTROLLED, OTHER IS CONSTANT POWER		
	SWITCH	44" A.F.F., U.N.O.	
	3-WAY SWITCH	44" A.F.F., U.N.O.	
	DIMMER SWITCH	44" A.F.F., U.N.O.	
	RECESSED CAN FIXTURE	CLG. MTD., U.N.O.	
	RECESSED CAN FIXTURE- WET LOCATION	CLG. MTD., U.N.O.	
	CEILING-MTD. FIXTURE	CLG. MTD., U.N.O.	
	CEILING-MTD. FIXTURE- WET LOCATION	CLG. MTD., U.N.O.	
	WALL-MTD. FIXTURE	AS NOTED	MOUNT PER PLANS & ELEVATIONS
	WALL-MTD. FIXTURE- WET LOCATION	AS NOTED	MOUNT PER PLANS & ELEVATIONS
	PENDANT FIXTURE		MOUNT PER PLANS & ELEVATIONS
	WALLWASHER FIXTURE	CLG. MTD., U.N.O.	
	DIRECTIONAL PENDANT FIXTURE		TECH LIGHTING 700 SCANIA FREEJACK FIXTURES
	LED LINEAR LIGHT		
	LED PUCK LIGHT		
	LIGHTING TRANSFORMER		
	JUNCTION BOX		
	CEILING-MTD. JUNCTION BOX	CLG. MTD., U.N.O.	
	WALL-MTD. JUNCTION BOX		MOUNT PER PLANS & ELEVATIONS
	TELEPHONE OUTLET	12" A.F.F., U.N.O.	
	DATA OUTLET	12" A.F.F., U.N.O.	
	CABLE TELEVISION	12" A.F.F., U.N.O.	
	THERMOSTAT	48" A.F.F., U.N.O.	
	DOORBELL	48" A.F.F., U.N.O.	
	EXHAUST FAN		
	WALL-MTD. EXHAUST FAN		
	SMOKE DETECTOR		HARDWIRED, CEILING-MTD. OR WALL-MTD. 12" BELOW CEILING HEIGHT, U.N.O.
	CARBON MONOXIDE DETECTOR		HARDWIRED
	ELECTRICAL PANEL BOARD		
	GARAGE DOOR OPENER		
	CEILING FAN W/O LIGHT		ELECTRICAL BOX RATED FOR MIN. 50 LBS.

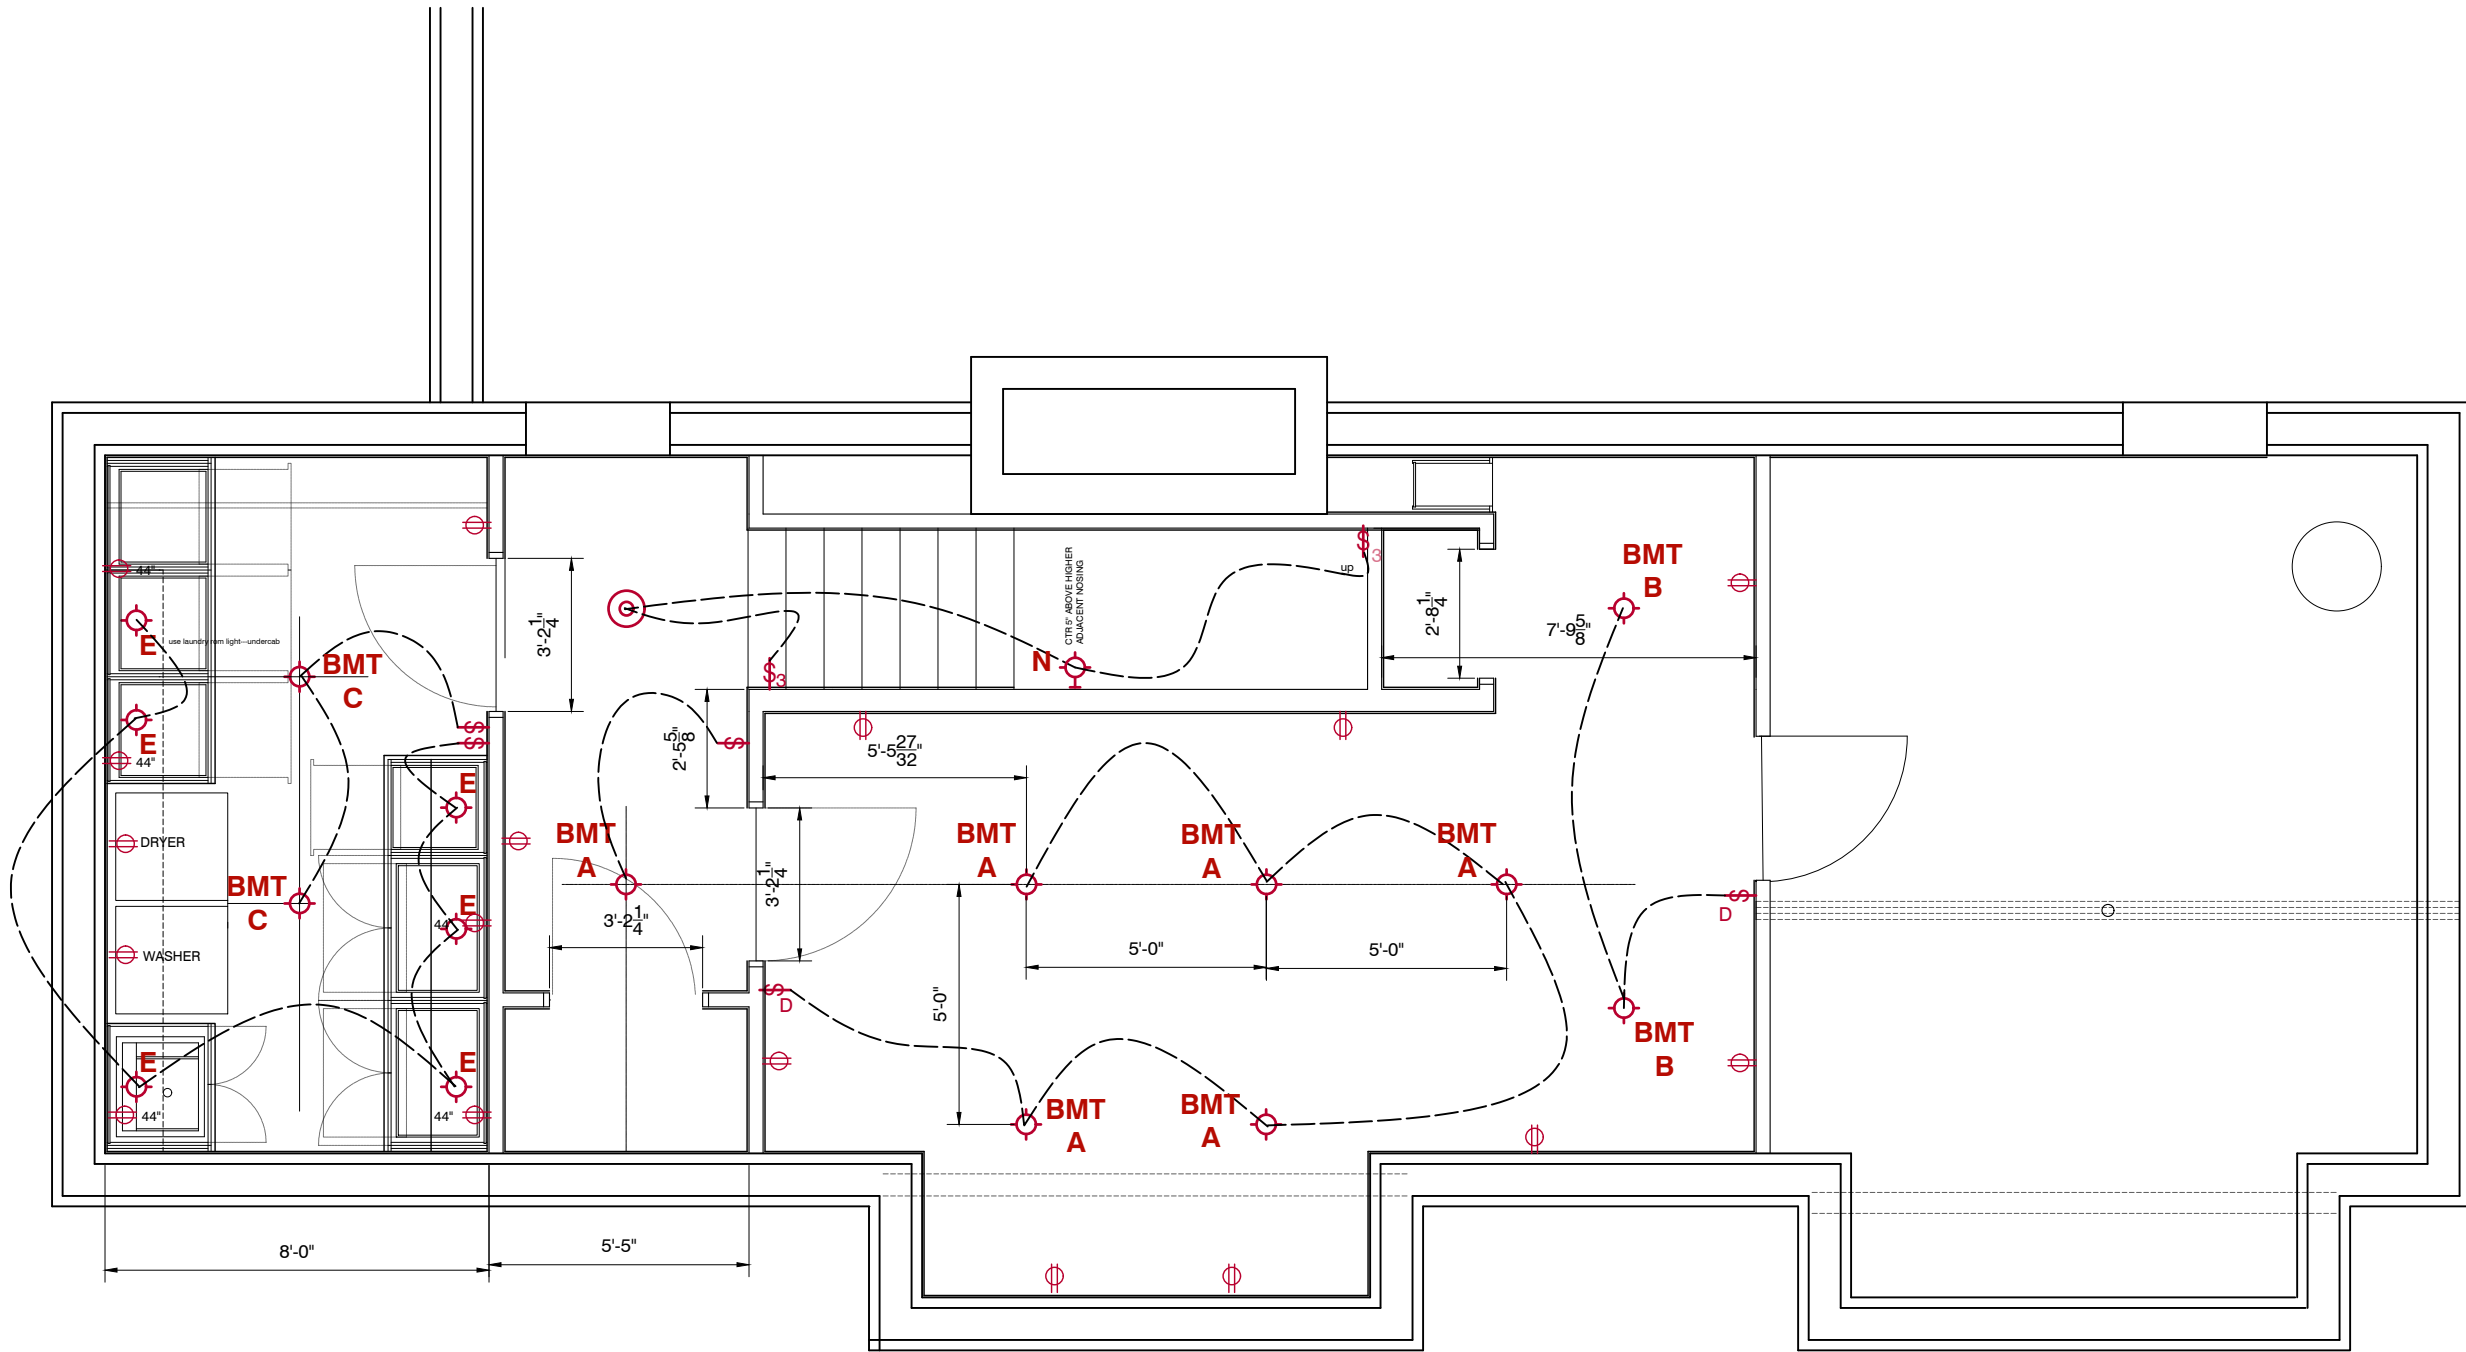

1 BASEMENT FLOOR ELEC
1/4" = 1' - 0"